
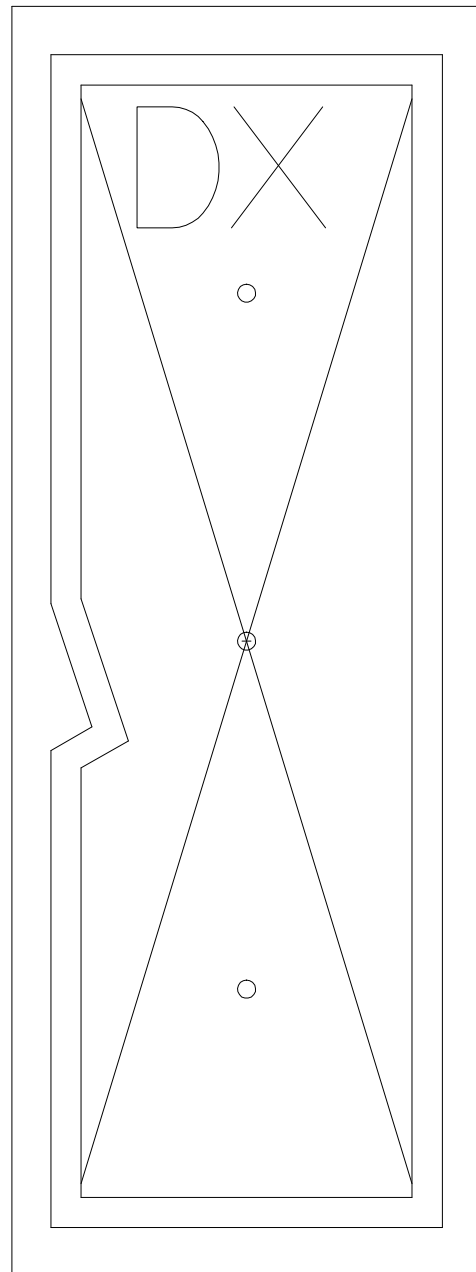


RIF.	QUANTITA'	ESSENZA	MODELLO	CONSEGNA ENTRO IL
MANO APERTURA		BATTENTE		
SX ☐	DX ☐	☐	☐	

PANNELLI TRAFORATI PER UNA ANTA 807X2099
(SPESSORE 5.25)

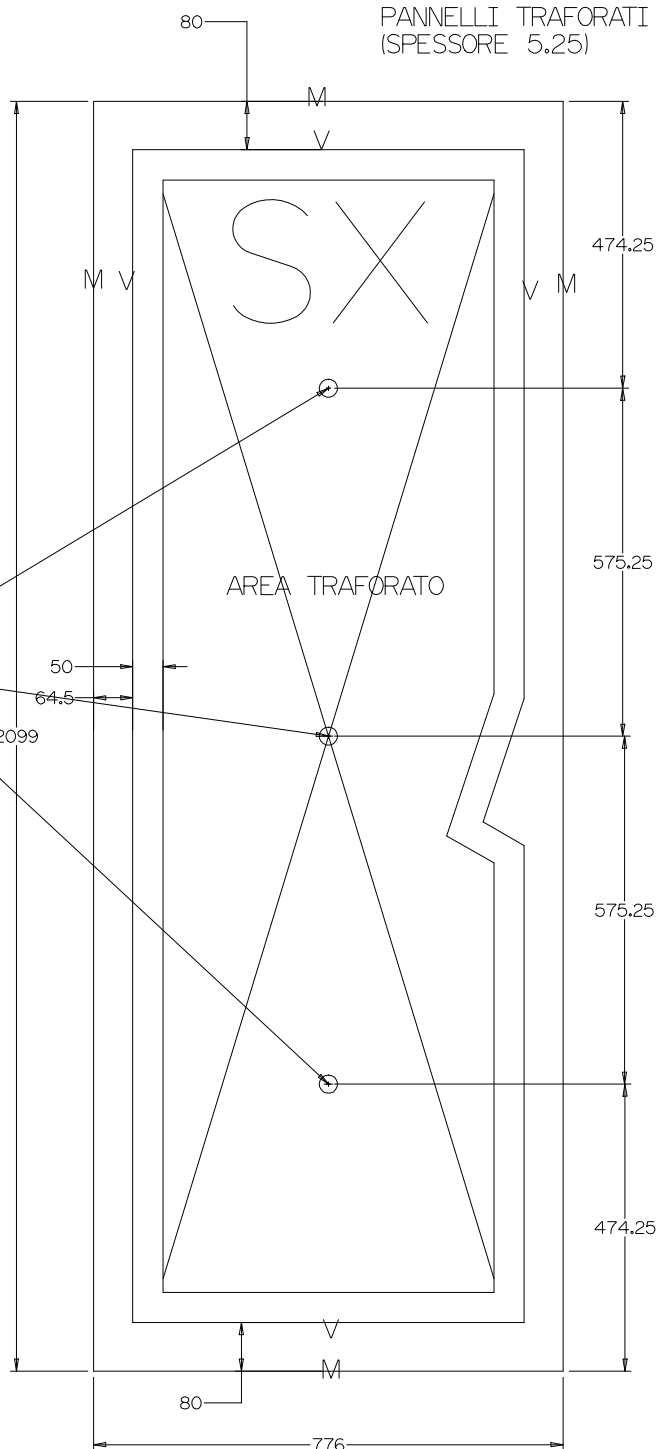

LEGENDA LAVORAZIONI LASER:

[V] = FUGA A V DI 1.5-3 mm largh.

[X] = AREA TRAFORO SECONDO SPECIFICHE ARCHITETTO

LEGENDA LAVORAZIONI MANUALI

[M] = SPIGOLARE MANUALMENTE

Ufficio tecnico: TOSCOCORNICI PORTE tel. 0577-68.54.26 - fax 0577-68.64.29 e-mail: tecnico@toscocornici.it - web: www.toscocornici.it	documento:	data:
	PORTALAPORTA_STD-V_LASER responsabile tecnico: B.Stefano	16/4/12 scala: 1 : 10